

EXHIBIT A.7 FLOOR MAP


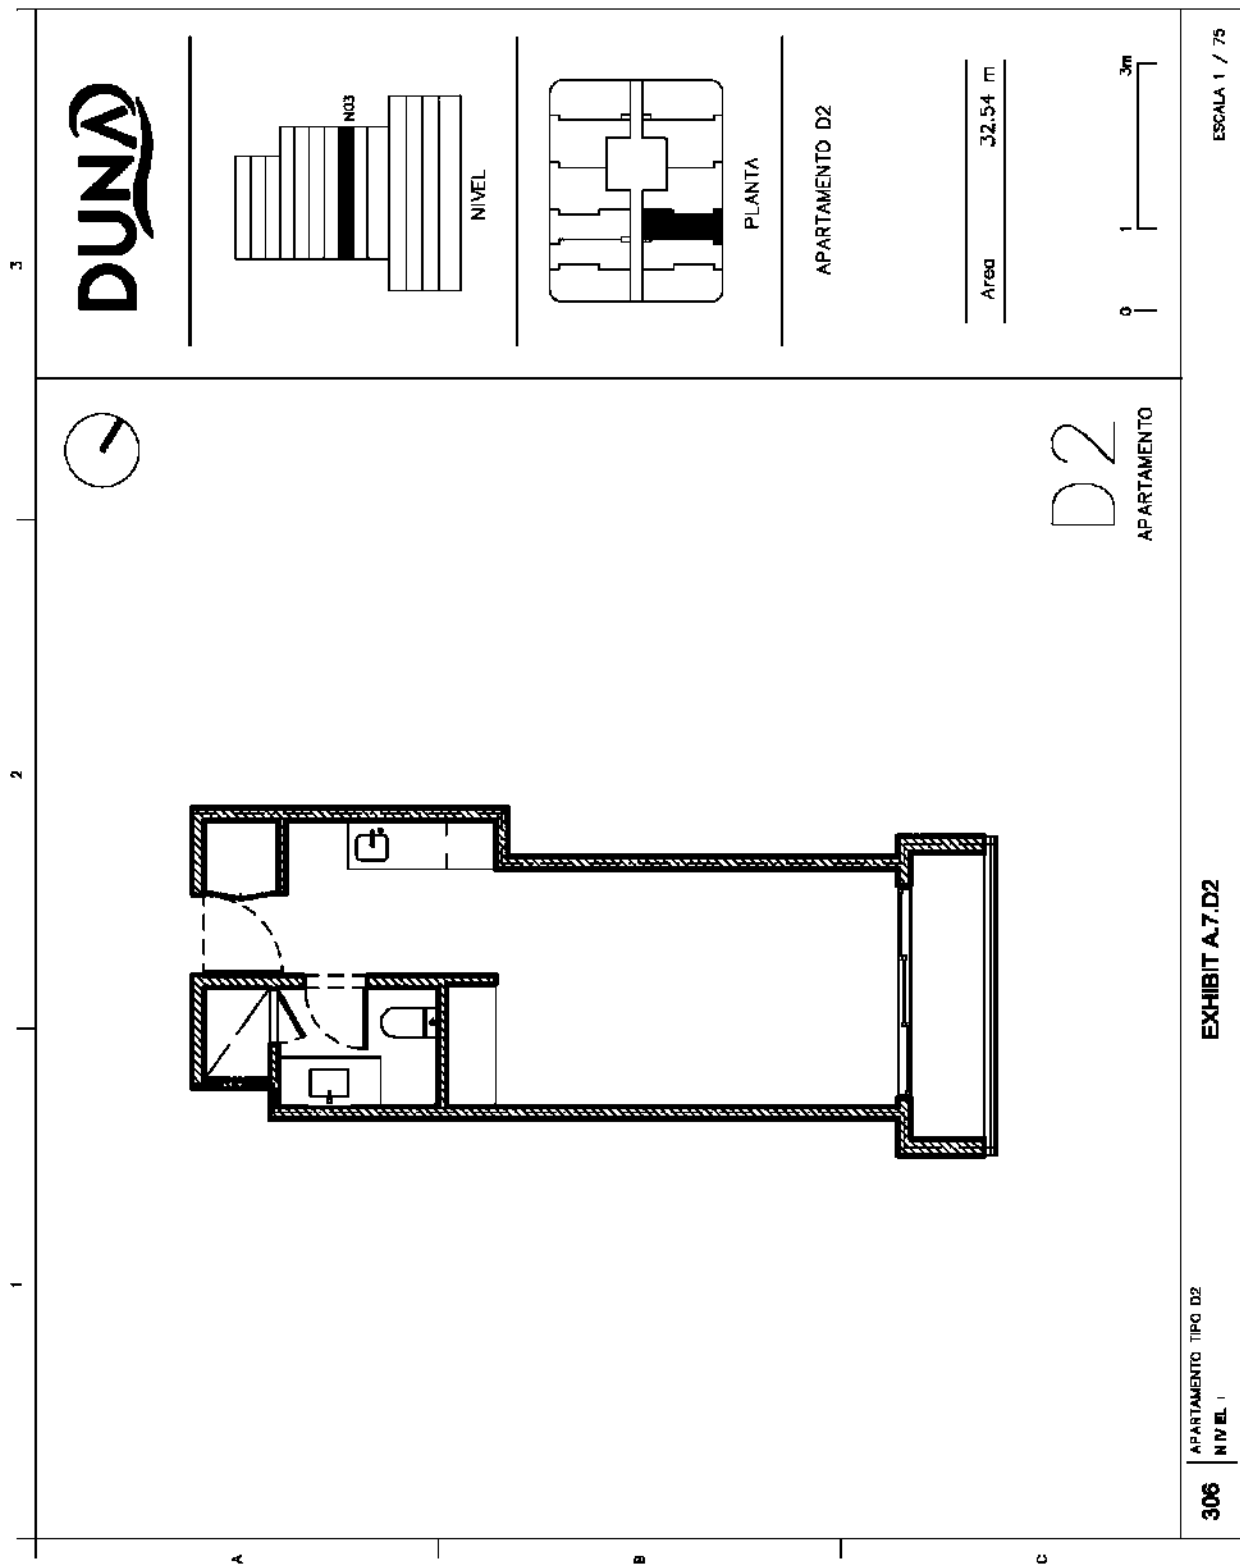


EXHIBIT A.7 FLOOR MAP

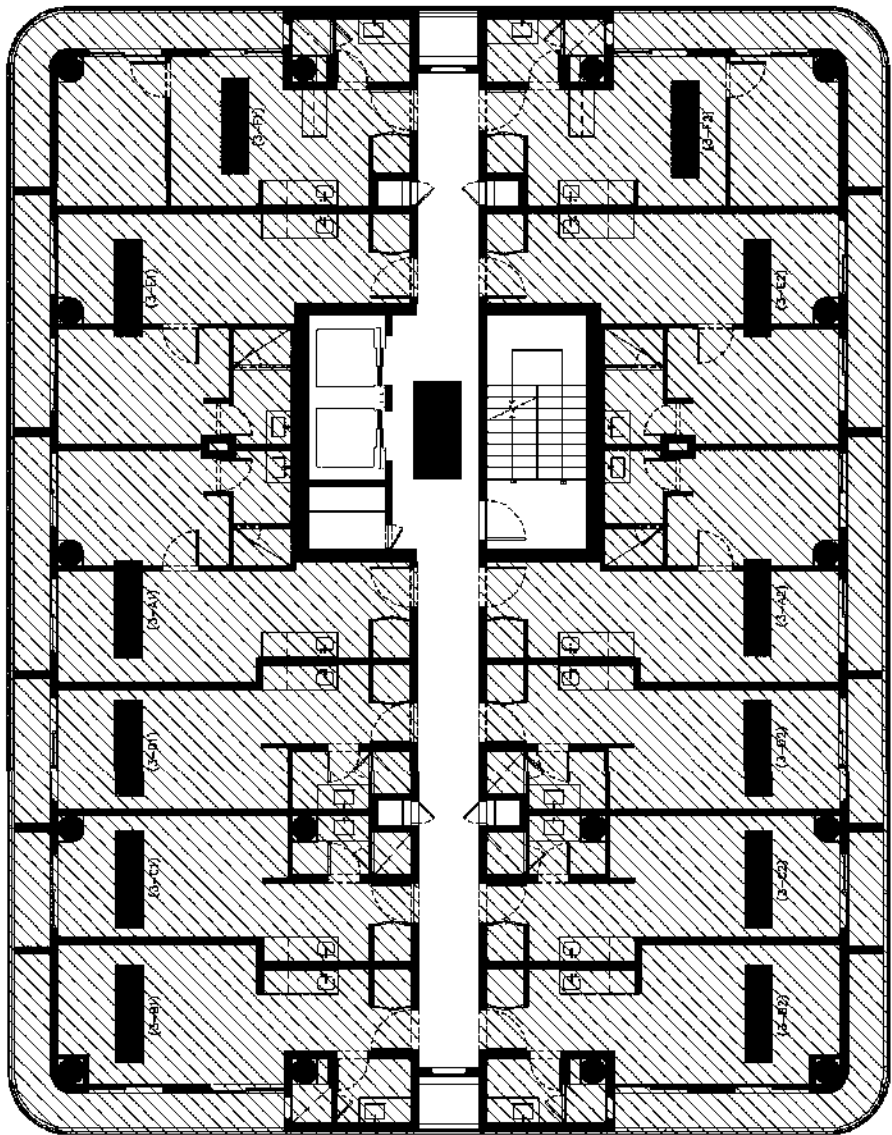

CLASSIFICATION	DESIGNATION	AREA (M2)
UNITIZED (RESIDENTIAL)	301	41.55
UNITIZED (RESIDENTIAL)	302	41.55
UNITIZED (RESIDENTIAL)	303	31.07
UNITIZED (RESIDENTIAL)	304	31.07
UNITIZED (RESIDENTIAL)	305	32.54
UNITIZED (RESIDENTIAL)	306	32.54
UNITIZED (RESIDENTIAL)	307	45.67
UNITIZED (RESIDENTIAL)	308	45.67
UNITIZED (RESIDENTIAL)	309	45.66
UNITIZED (RESIDENTIAL)	310	45.69
UNITIZED (RESIDENTIAL)	311	45.03
UNITIZED (RESIDENTIAL)	312	45.03
COMMON AREA	3-CA	84.34

QUINA TOWER #1
LOCATION: ISLAS DE LA BAHIA, ROATAN, HONDURAS
Ex-A.7
LEVEL: 3
DATE: MARCH 2024
OWNER: DIONYSIUS LLC

Ex.A.7 – LEVEL 3