



EXHIBIT A.8 FLOOR MAP

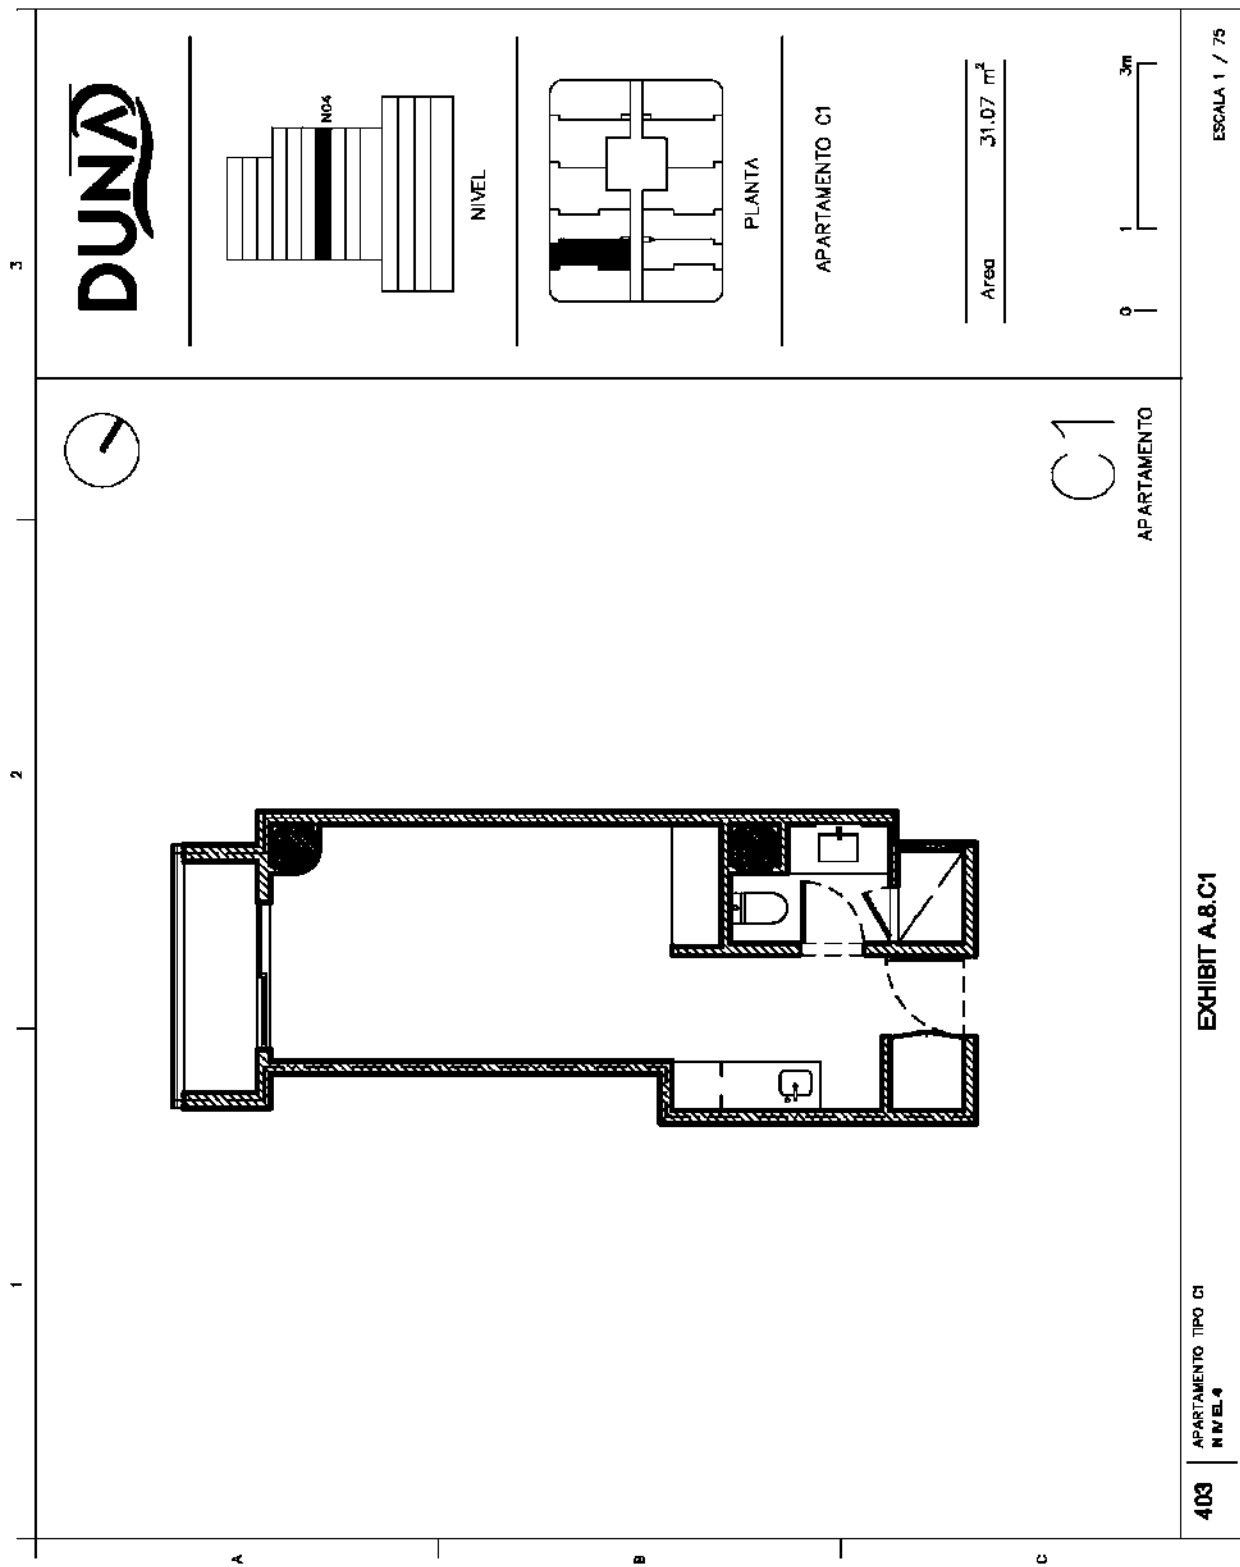

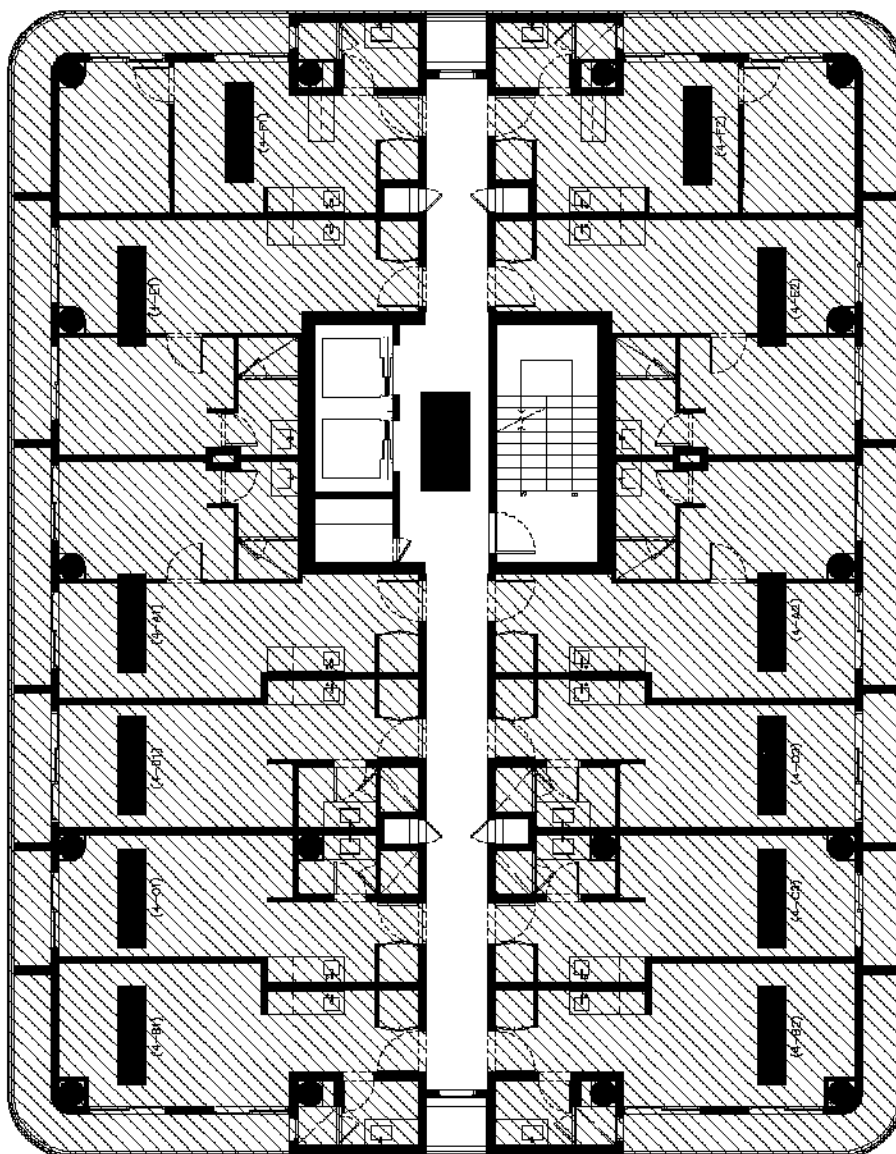

	CLASSIFICATION	DESIGNATION	AREA A (M2)
	UNITIZED (RESIDENTIAL)	401	41.50
	UNITIZED (RESIDENTIAL)	402	41.56
	UNITIZED (RESIDENTIAL)	403	31.07
	UNITIZED (RESIDENTIAL)	404	31.07
	UNITIZED (RESIDENTIAL)	405	32.54
	UNITIZED (RESIDENTIAL)	408	32.54
	UNITIZED (RESIDENTIAL)	407	45.67
	UNITIZED (RESIDENTIAL)	408	45.67
	UNITIZED (RESIDENTIAL)	409	45.68
	UNITIZED (RESIDENTIAL)	410	45.68
	UNITIZED (RESIDENTIAL)	411	45.03
	UNITIZED (RESIDENTIAL)	412	45.03
	COMMON ARE A	4-C/A	84.34

DUNA TOWER #1

LOCATION:
ISLAS DE LA BAHIA.
ROATÁN, HONDURAS

三、 A, B

EVEL: 4

DATE: MARCH 2024

OWNER:
DIONYSIUS LLC

EX.A.8 - LEVEL 4