

EXHIBIT A.9 FLOOR MAP


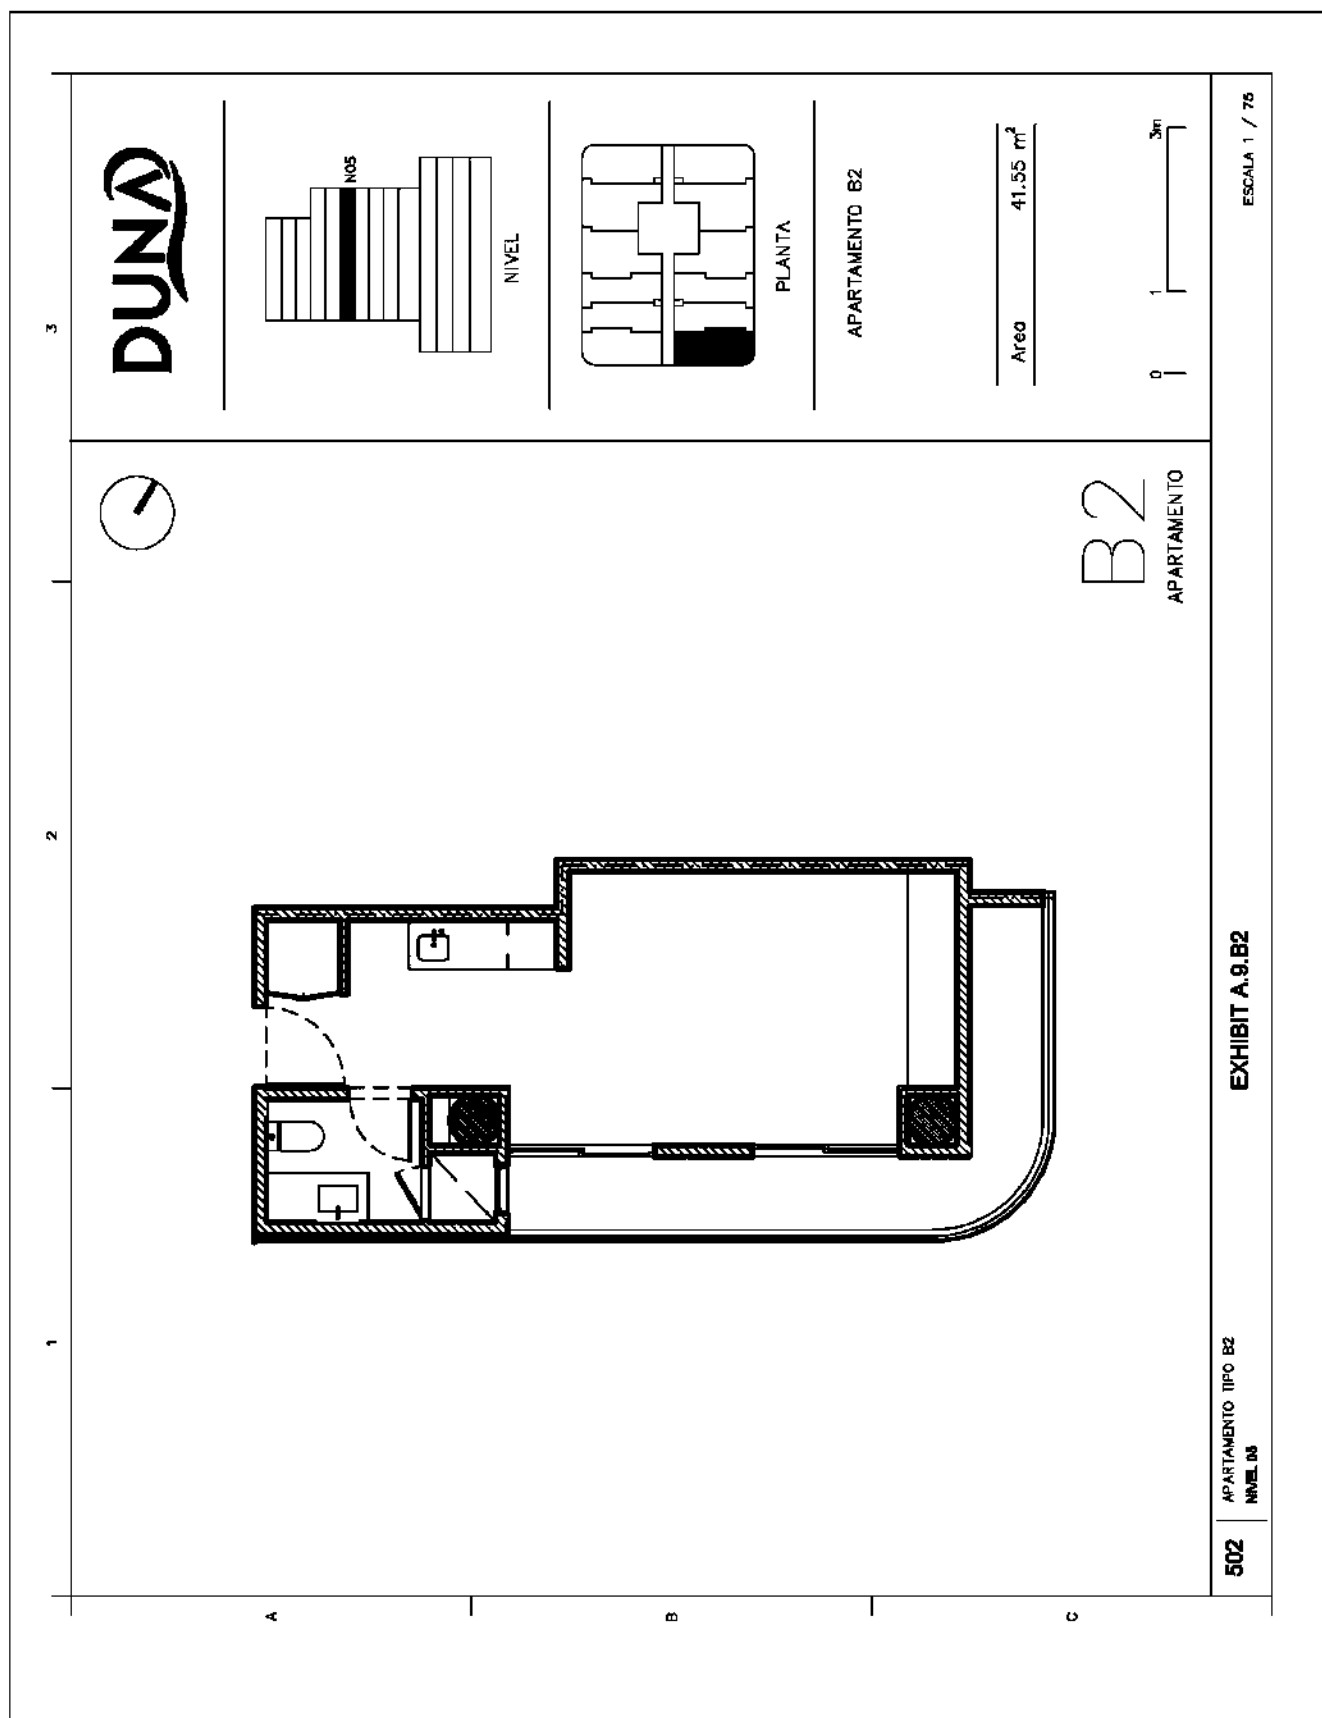


EXHIBIT A.9 FLOOR MAP

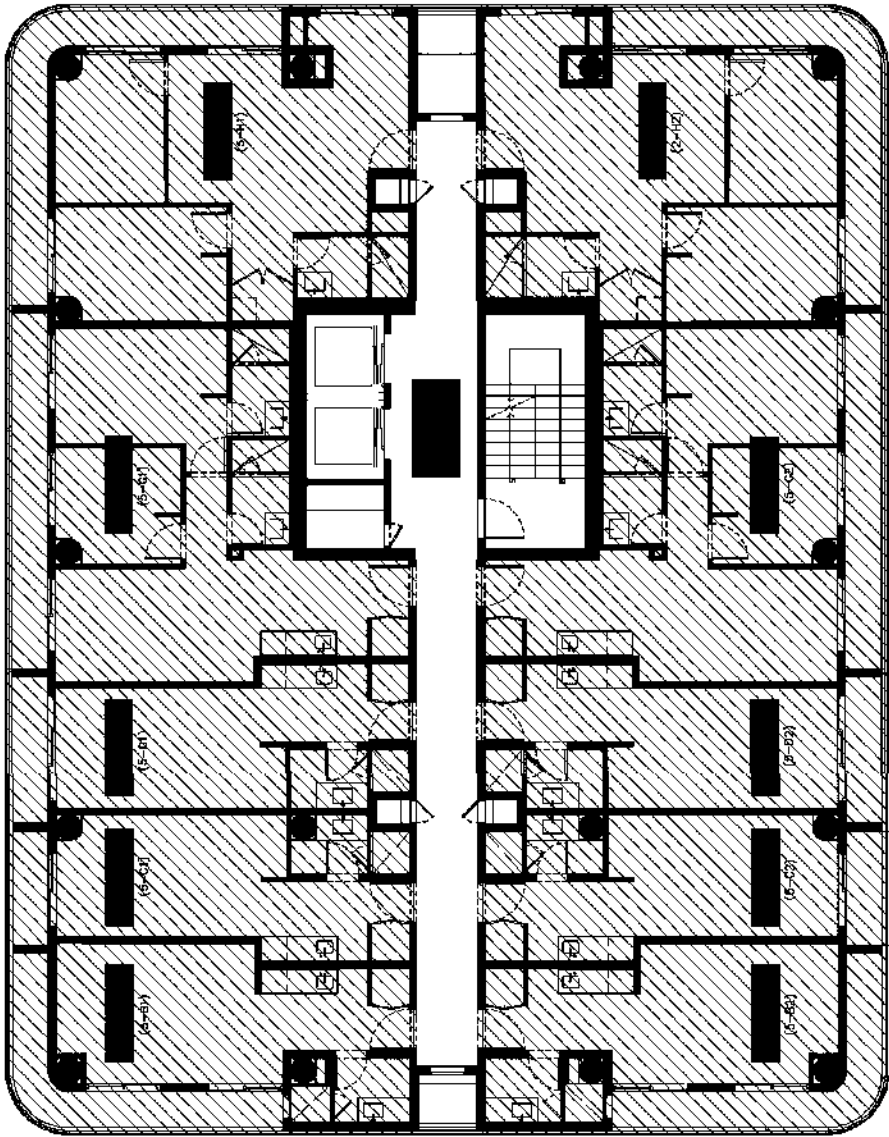

CLASSIFICATION	DESIGNATION	AREA (M2)
UNITIZED (RESIDENTIAL)	501	41.55
UNITIZED (RESIDENTIAL)	502	41.55
UNITIZED (RESIDENTIAL)	503	31.07
UNITIZED (RESIDENTIAL)	504	31.07
UNITIZED (RESIDENTIAL)	505	32.54
UNITIZED (RESIDENTIAL)	506	32.54
UNITIZED (RESIDENTIAL)	507	65.84
UNITIZED (RESIDENTIAL)	508	65.84
UNITIZED (RESIDENTIAL)	509	71.13
UNITIZED (RESIDENTIAL)	510	71.13
COMMON AREA	5-CA	64.14

DUNA TOWER #1
LOCATION: ISLAS DE LA BAHIA, ROTAN, HONDURAS
Ex.A.8
LEVEL: LEVEL 5
DATE: MARCH 2024
OWNER: UNIVERSUS LLC

Ex.A.9 – LEVEL 5