

EXHIBIT A.11 FLOOR MAP


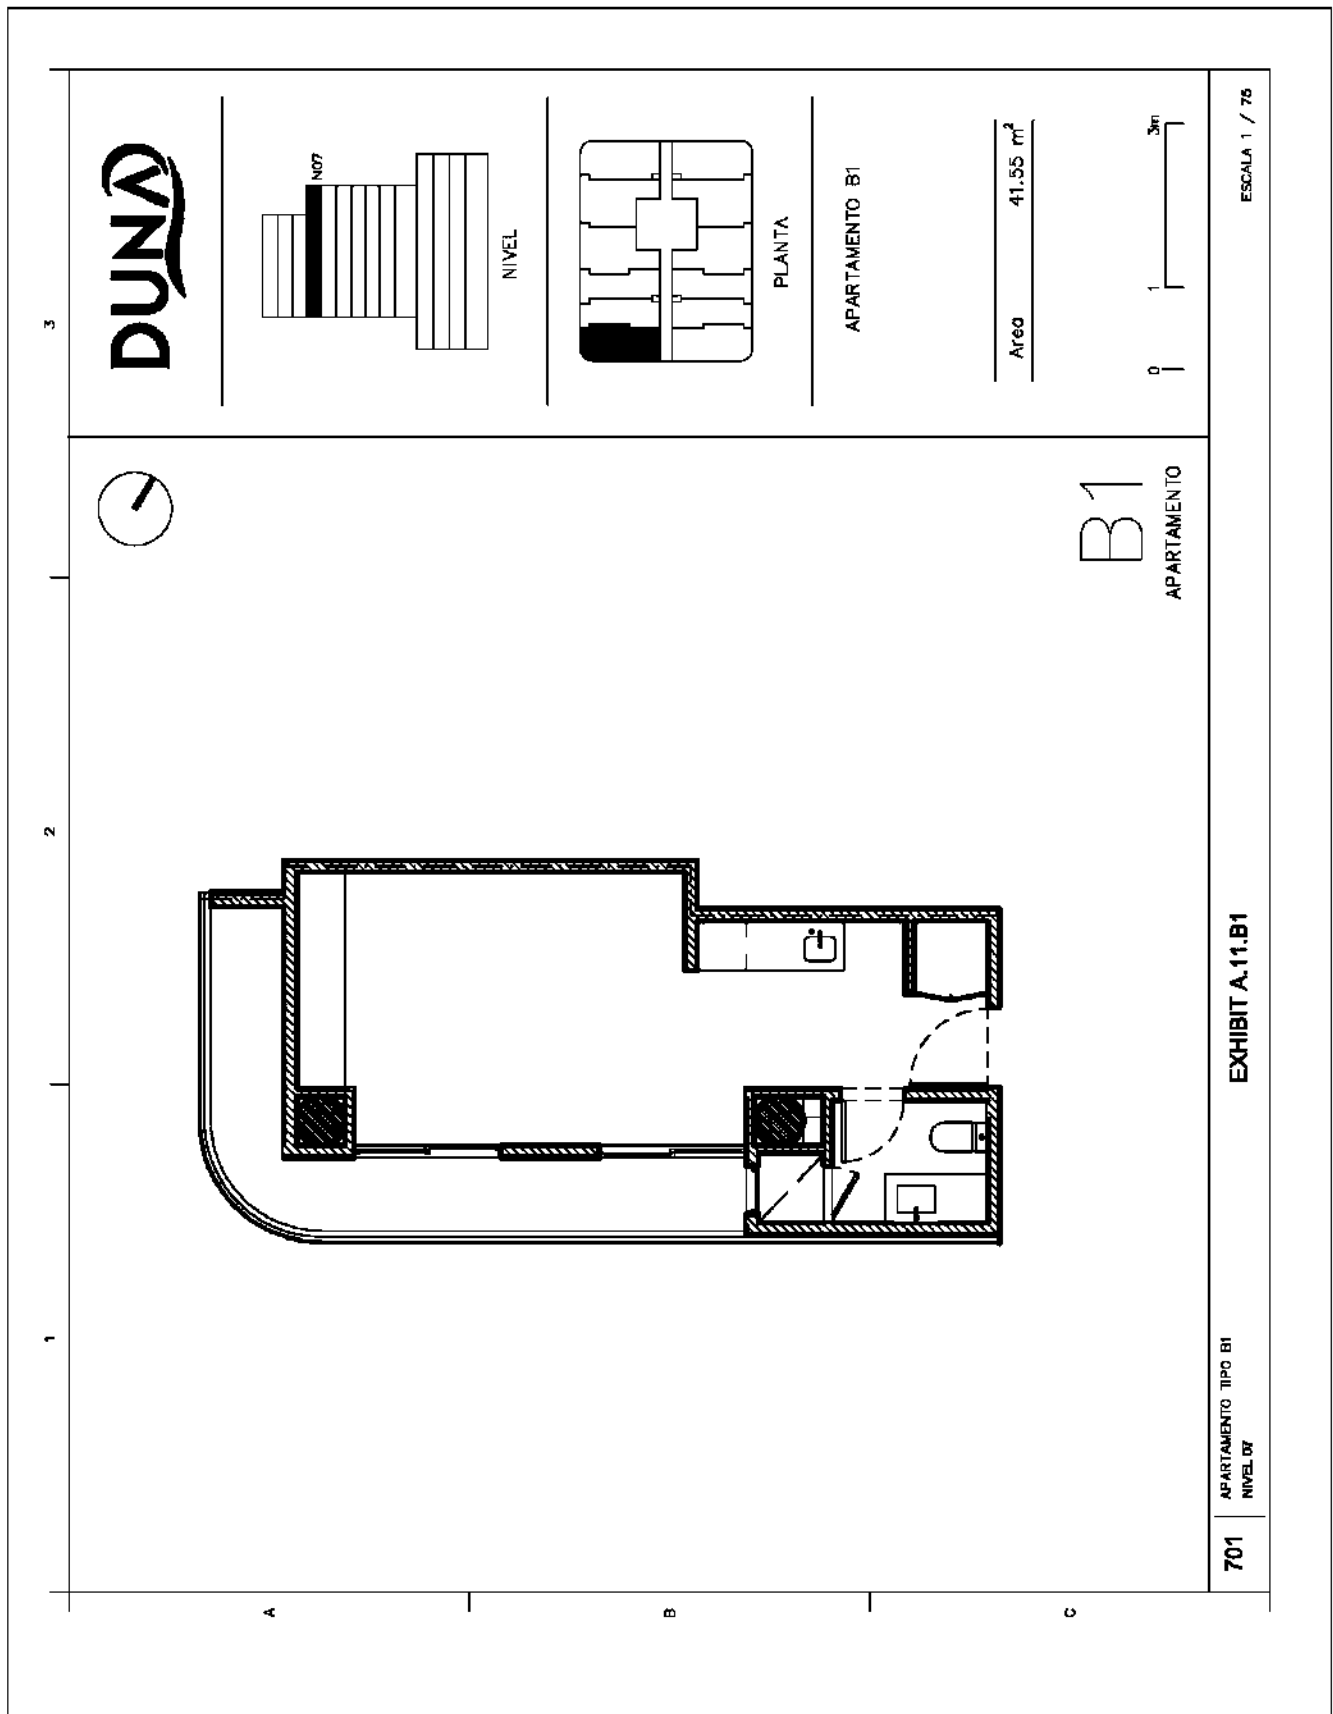


EXHIBIT A.11 FLOOR MAP

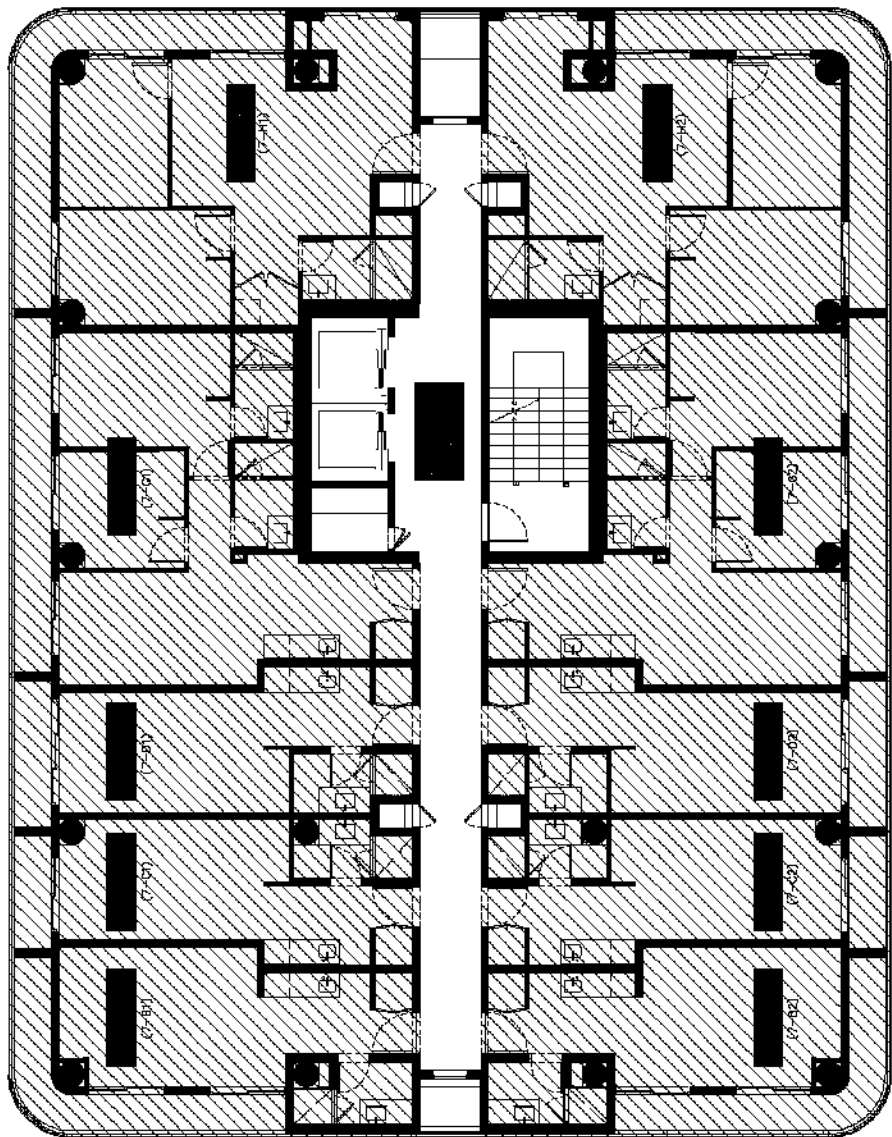

CLASSIFICATION	DESIGNATION	AREA (M2)
UNITIZED (RESIDENTIAL)	701	41.55
UNITIZED (RESIDENTIAL)	702	41.55
UNITIZED (RESIDENTIAL)	703	31.07
UNITIZED (RESIDENTIAL)	704	31.07
UNITIZED (RESIDENTIAL)	705	32.54
UNITIZED (RESIDENTIAL)	706	32.54
UNITIZED (RESIDENTIAL)	707	65.54
UNITIZED (RESIDENTIAL)	708	65.54
UNITIZED (RESIDENTIAL)	709	71.13
UNITIZED (RESIDENTIAL)	710	71.13
COMMON AREA	7-CA	84.14

DUNA TOWER #1
LOCATION: ISLAS DE LA BAHIA, ROTATAN, HONDURAS
Ex.A.11
LEVEL: LEVEL 7
DATE: MARCH 2024
OWNER: BUNYUS LLC

Ex.A.11 – LEVEL 7