

EXHIBIT A.13 FLOOR MAP


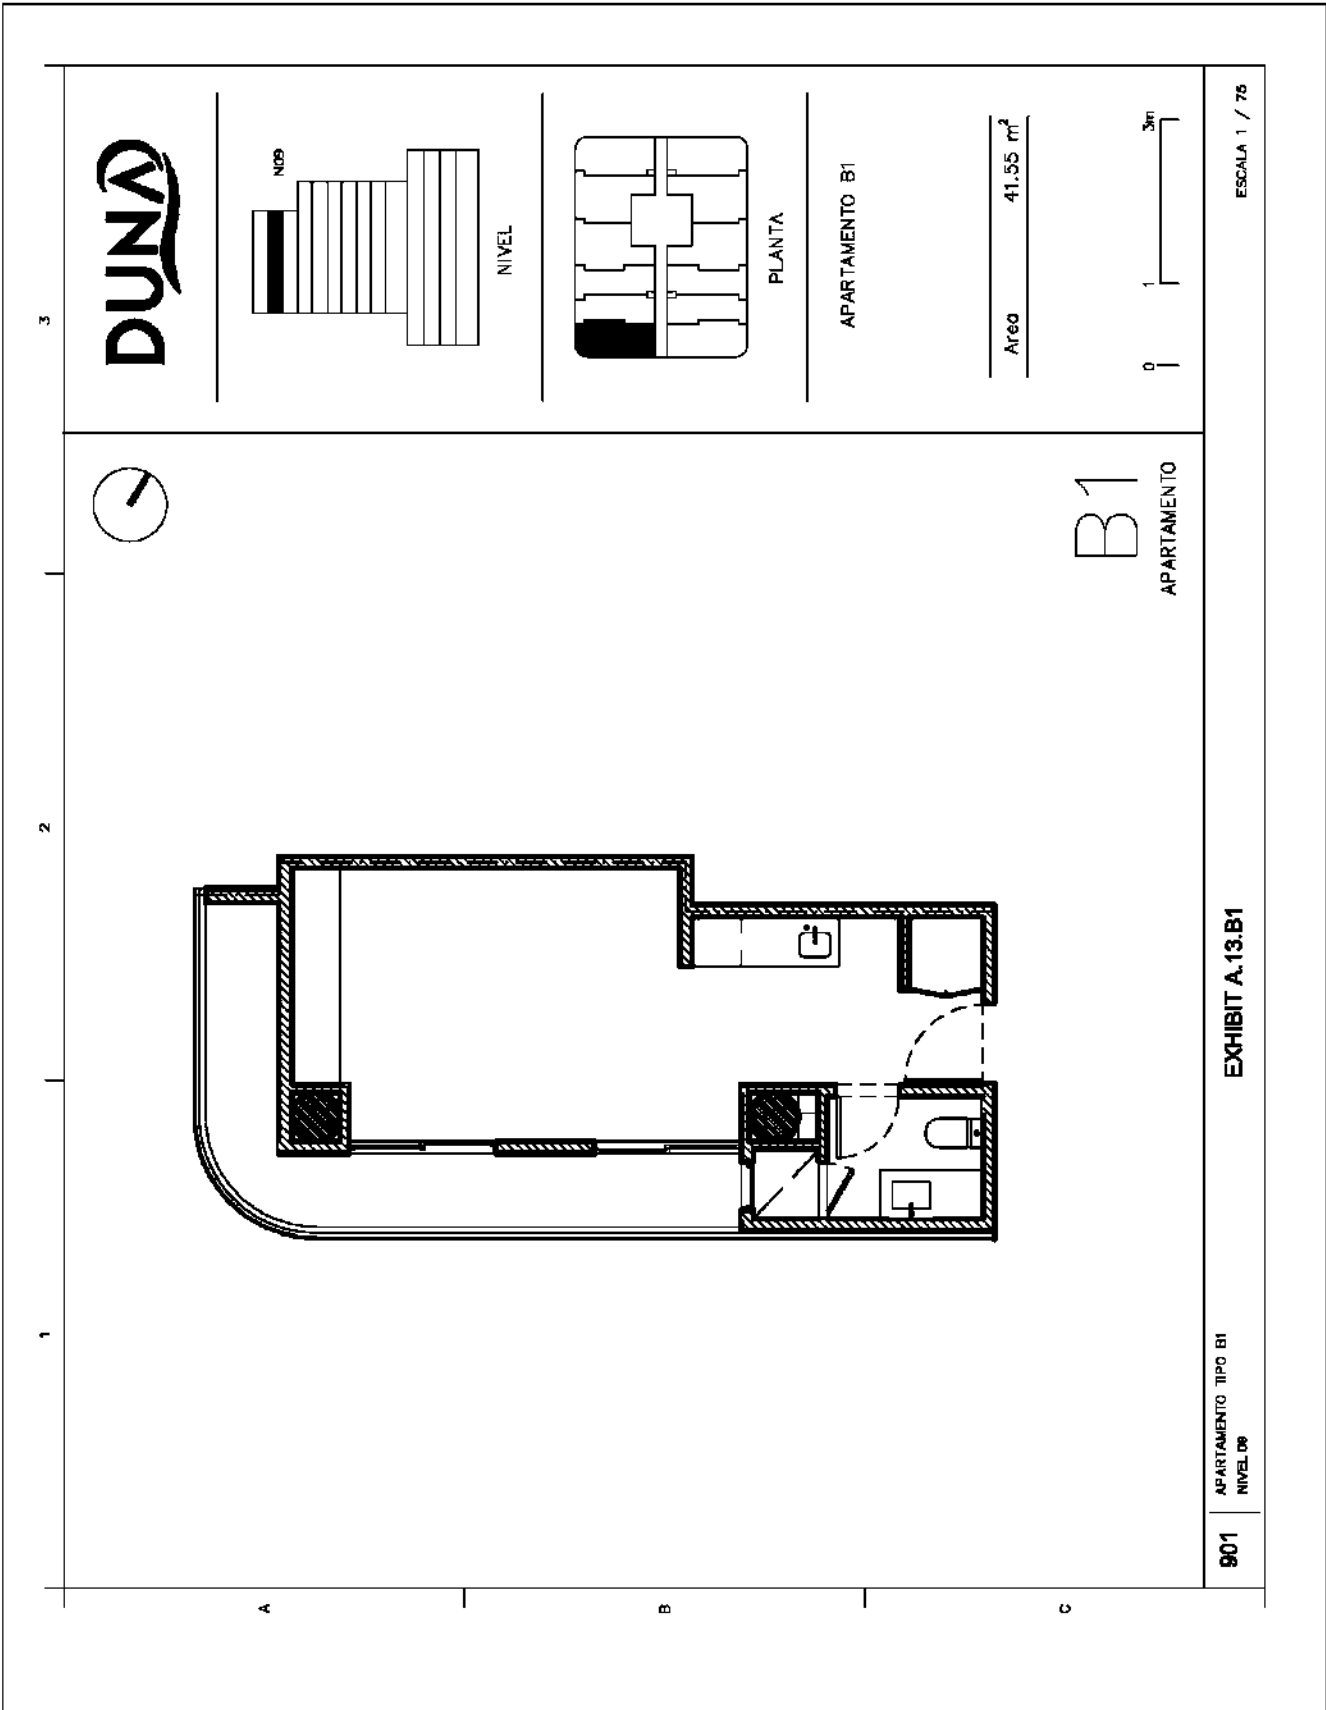


EXHIBIT A.13 FLOOR MAP

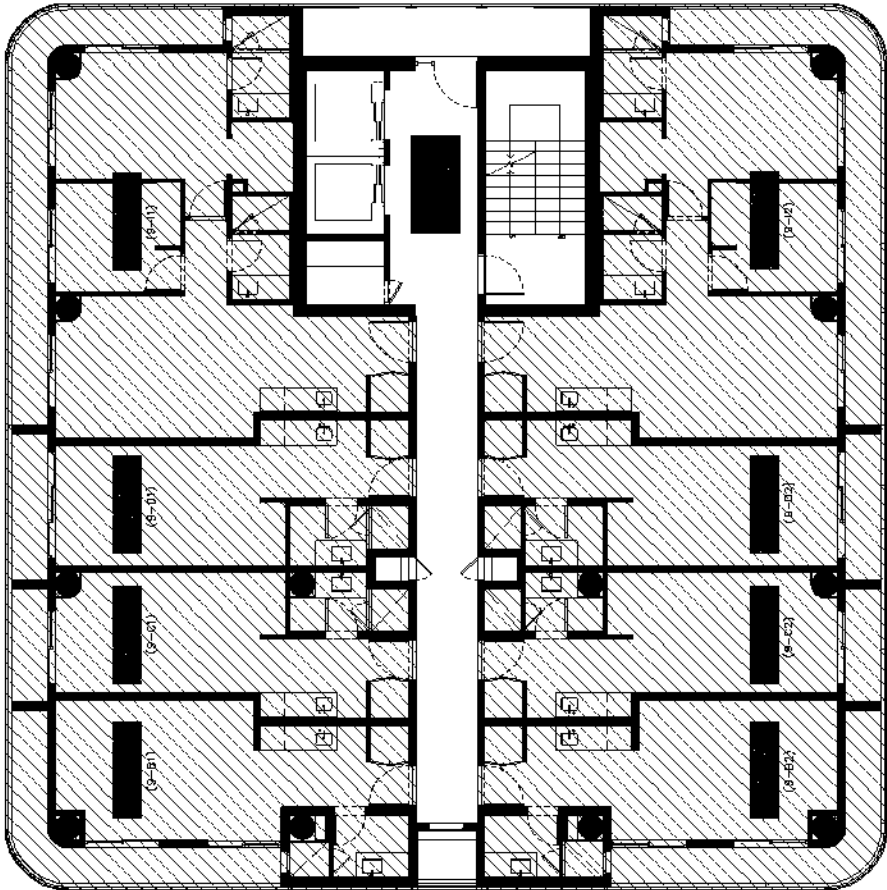

CLASSIFICATION	DESIGNATION	AREA (M2)
UNITIZED (RESIDENTIAL)	901	41.55
UNITIZED (RESIDENTIAL)	902	41.55
UNITIZED (RESIDENTIAL)	903	31.07
UNITIZED (RESIDENTIAL)	904	31.07
UNITIZED (RESIDENTIAL)	905	32.54
UNITIZED (RESIDENTIAL)	906	32.54
UNITIZED (RESIDENTIAL)	907	77.48
UNITIZED (RESIDENTIAL)	908	77.48
COMMON AREA	9-CA	80.14

DUNA TOWER #1
LOCATION: ISLAS DE LA BAHIA,
POATAN, HONDURAS

Ex-A.13

LEVEL: 9
DATE: MARCH 2024
OWNER: DUNYUS LLC

Ex.A.13 – LEVEL 9