

EXHIBIT A.13 FLOOR MAP


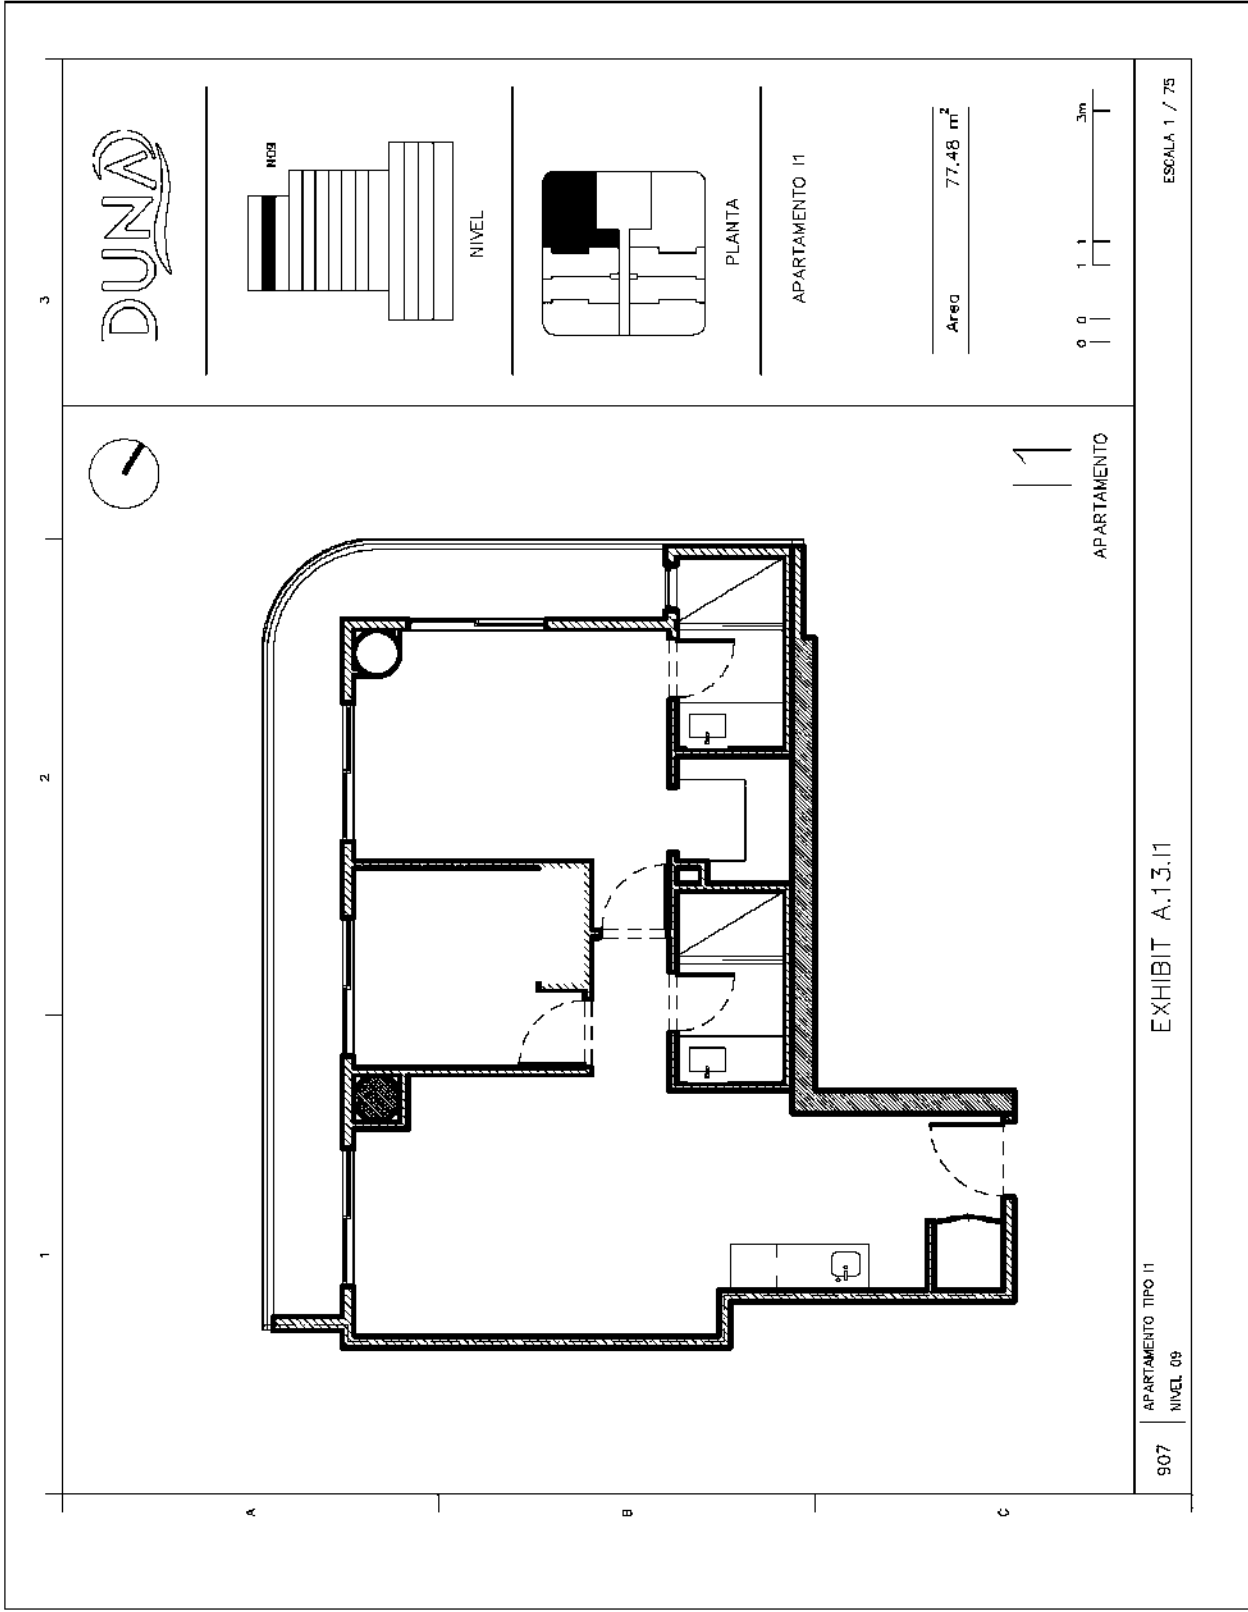


EXHIBIT A.13 FLOOR MAP

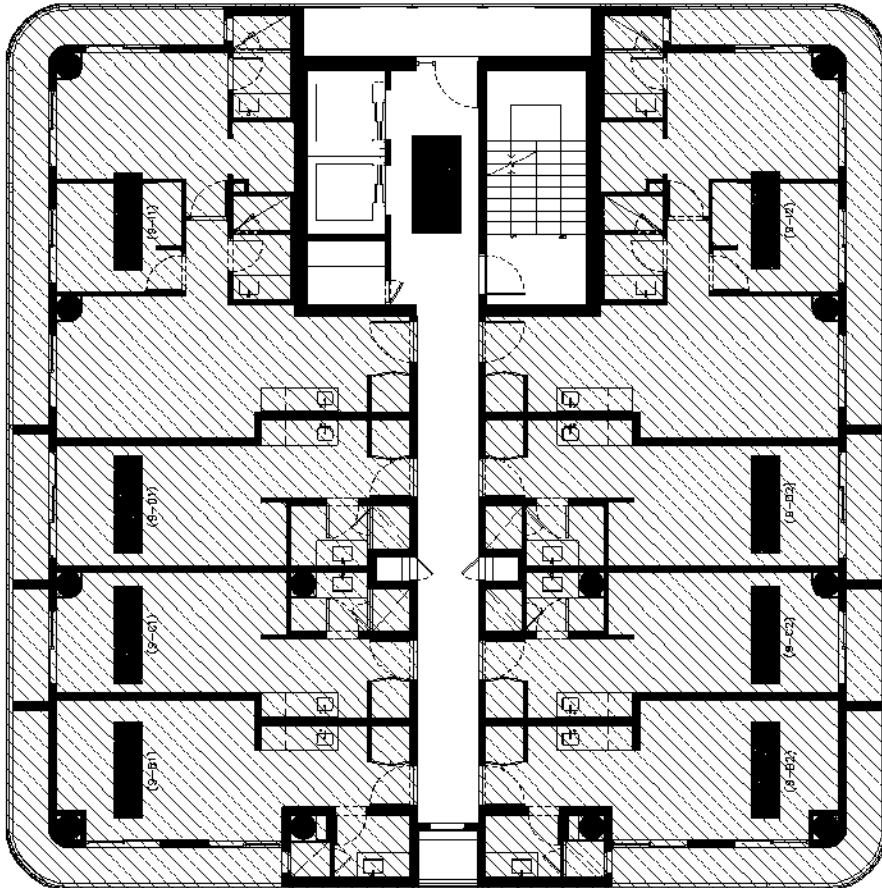

	CLASSIFICATION	DESIGNATION	AREA A (M ²)
	UNITIZED (RESIDENTIAL)	901	41.55
	UNITIZED (RESIDENTIAL)	902	41.53
	UNITIZED (RESIDENTIAL)	903	31.07
	UNITIZED (RESIDENTIAL)	904	31.07
	UNITIZED (RESIDENTIAL)	905	32.54
	UNITIZED (RESIDENTIAL)	906	32.54
	UNITIZED (RESIDENTIAL)	907	77.43
	UNITIZED (RESIDENTIAL)	908	77.48
	COMMON AREA	9-CA	80.14

DUNA TOWER 47

LOCATION:
ISLAS DE LA BAHIA,
BOATÁN HONDURAS

Ex.A.13

730

DATE: 11/28/2008

OWNER: _____

377 SNISANDID

Ex.A.13 – LEVEL 9