

EXHIBIT A.10 FLOOR MAP


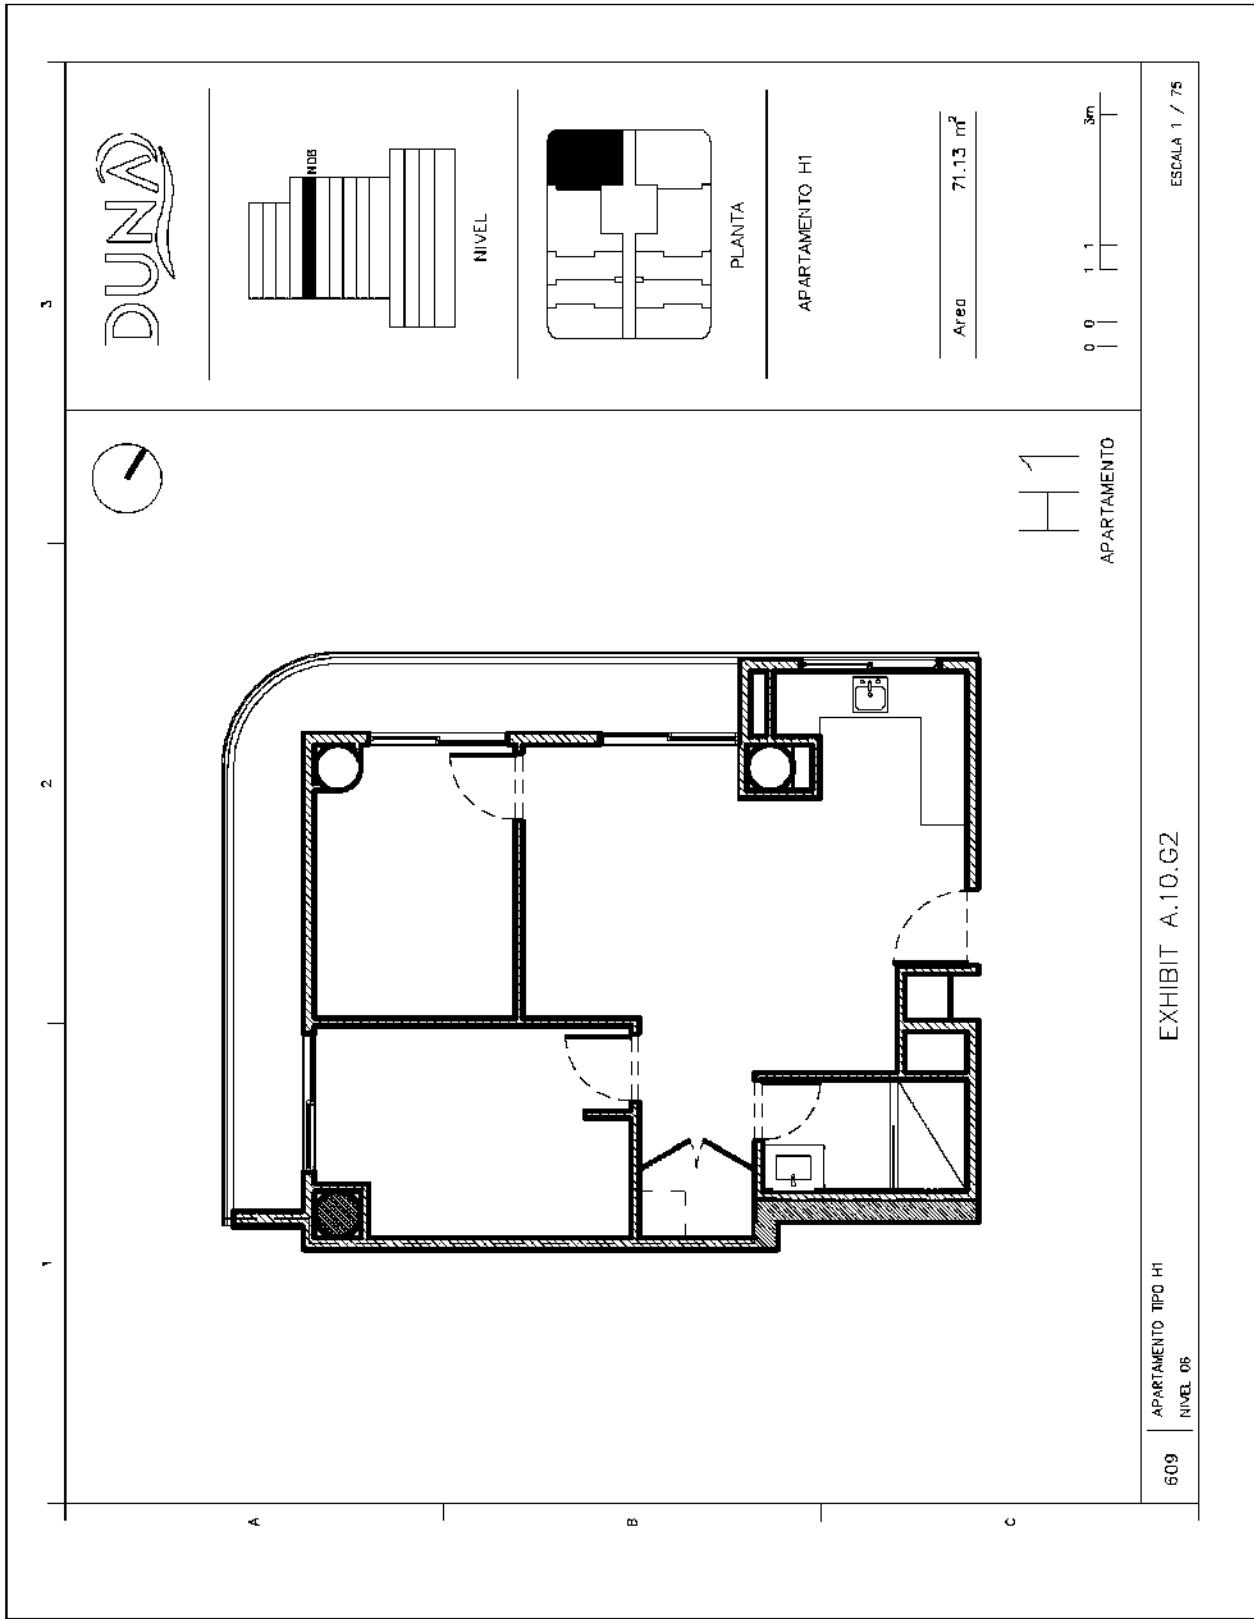


EXHIBIT A.10 FLOOR MAP

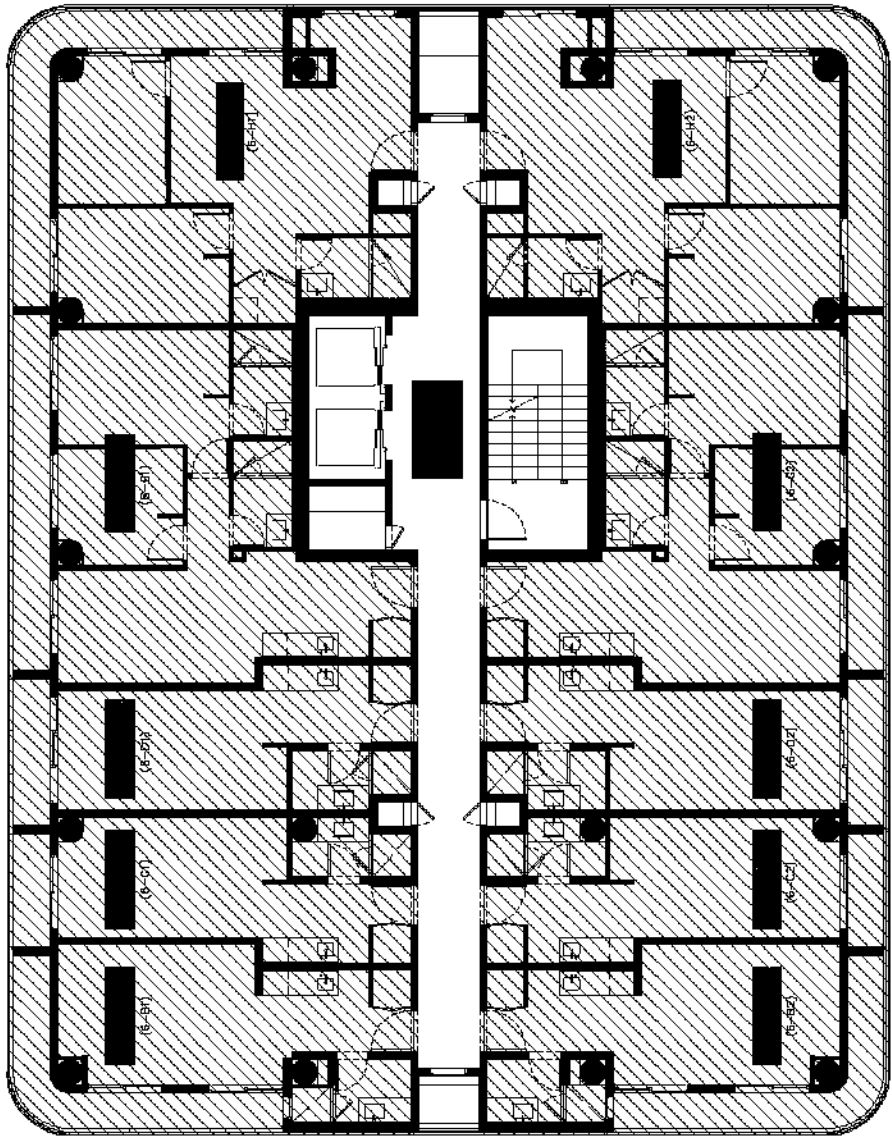

CLASSIFICATION	DESIGNATION	AREA (M2)
UNITIZED (RESIDENTIAL)	601	41.55
UNITIZED (RESIDENTIAL)	602	41.55
UNITIZED (RESIDENTIAL)	603	31.07
UNITIZED (RESIDENTIAL)	604	31.07
UNITIZED (RESIDENTIAL)	605	32.54
UNITIZED (RESIDENTIAL)	606	32.54
UNITIZED (RESIDENTIAL)	607	65.54
UNITIZED (RESIDENTIAL)	608	65.54
UNITIZED (RESIDENTIAL)	609	71.13
UNITIZED (RESIDENTIAL)	610	71.13
COMMON AREA	6-CA	84.14

DUNA TOWER #1
LOCATION: ISLAS DE LA BAHIA,
ROATAN, HONDURAS
Ex.A.10
LEVEL: LEVEL 6
DATE: MARCH 2024
OWNER: BURNBUSH LLC

Ex.A.10 – LEVEL 6