

EXHIBIT A.12 FLOOR MAP


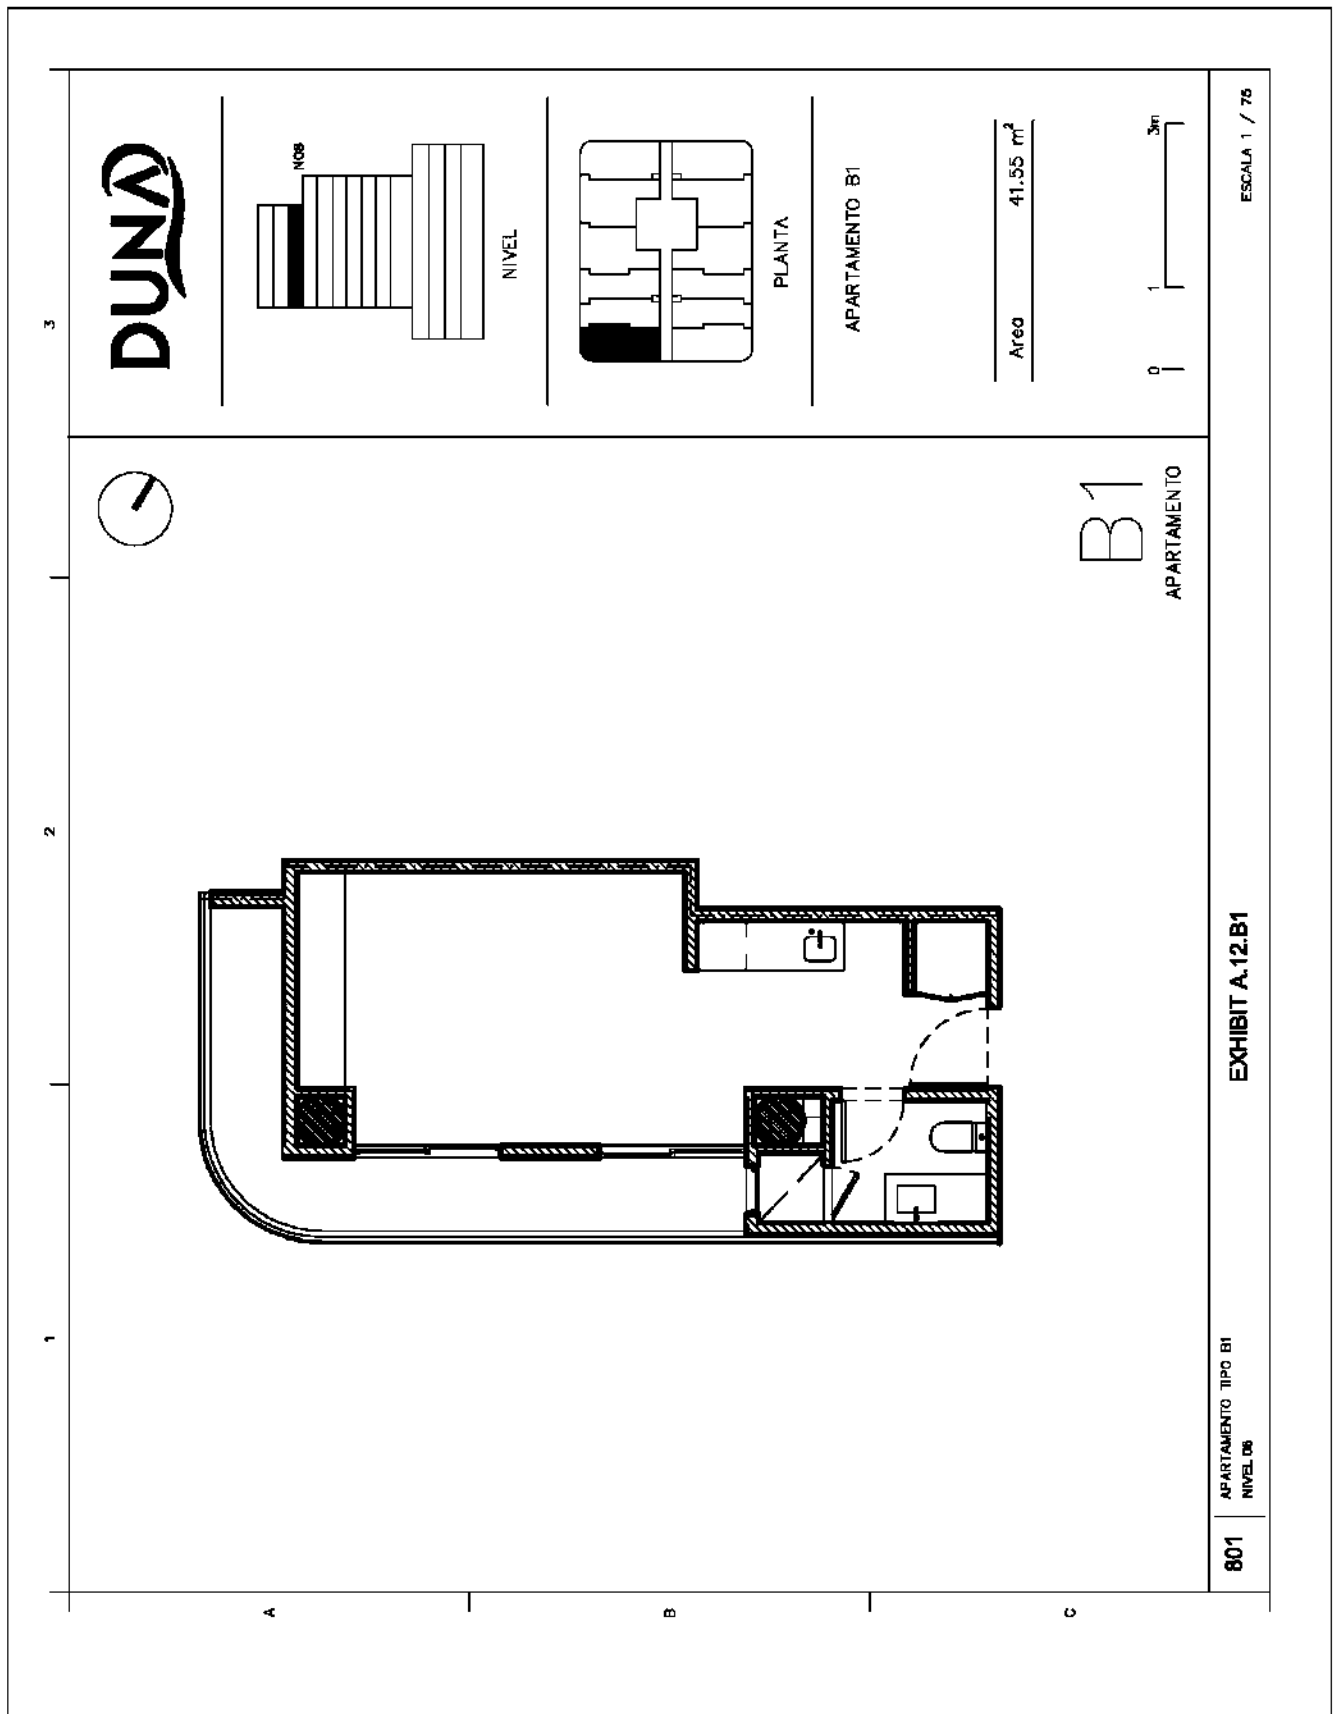


EXHIBIT A.12 FLOOR MAP

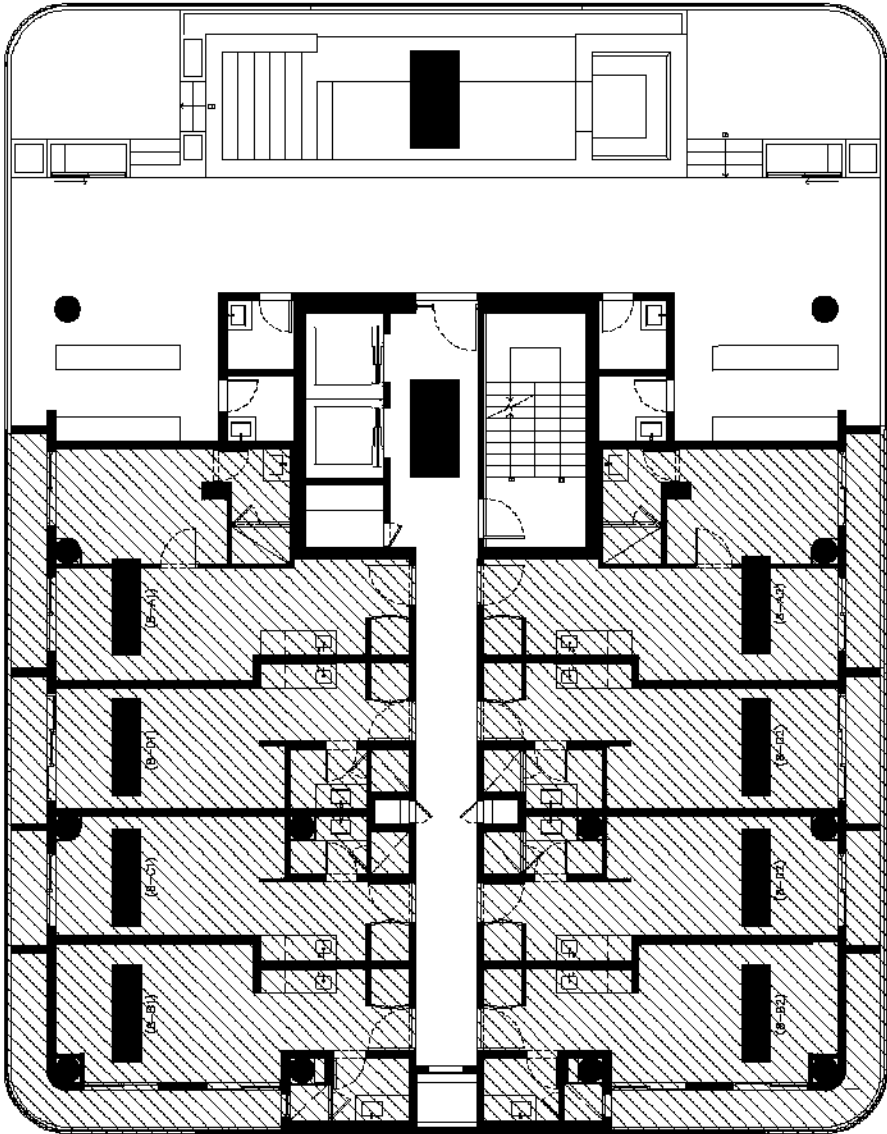

CLASSIFICATION	DESIGNATION	AREA (M2)
UNITIZED (RESIDENTIAL)	801	41.55
UNITIZED (RESIDENTIAL)	802	41.55
UNITIZED (RESIDENTIAL)	803	31.07
UNITIZED (RESIDENTIAL)	804	31.07
UNITIZED (RESIDENTIAL)	805	32.54
UNITIZED (RESIDENTIAL)	806	32.54
UNITIZED (RESIDENTIAL)	807	45.07
UNITIZED (RESIDENTIAL)	808	45.67
COMMON AREA	8-CA	638.23

DUNA TOWER #1
LOCATION: ISLAS DE LA BAHIA, ROTATAN, HONDURAS
Ex.A.12
LEVEL: 8
DATE: MARCH 2024
OWNER: BOUTSIJUS LLC

Ex.A.12 – LEVEL 8